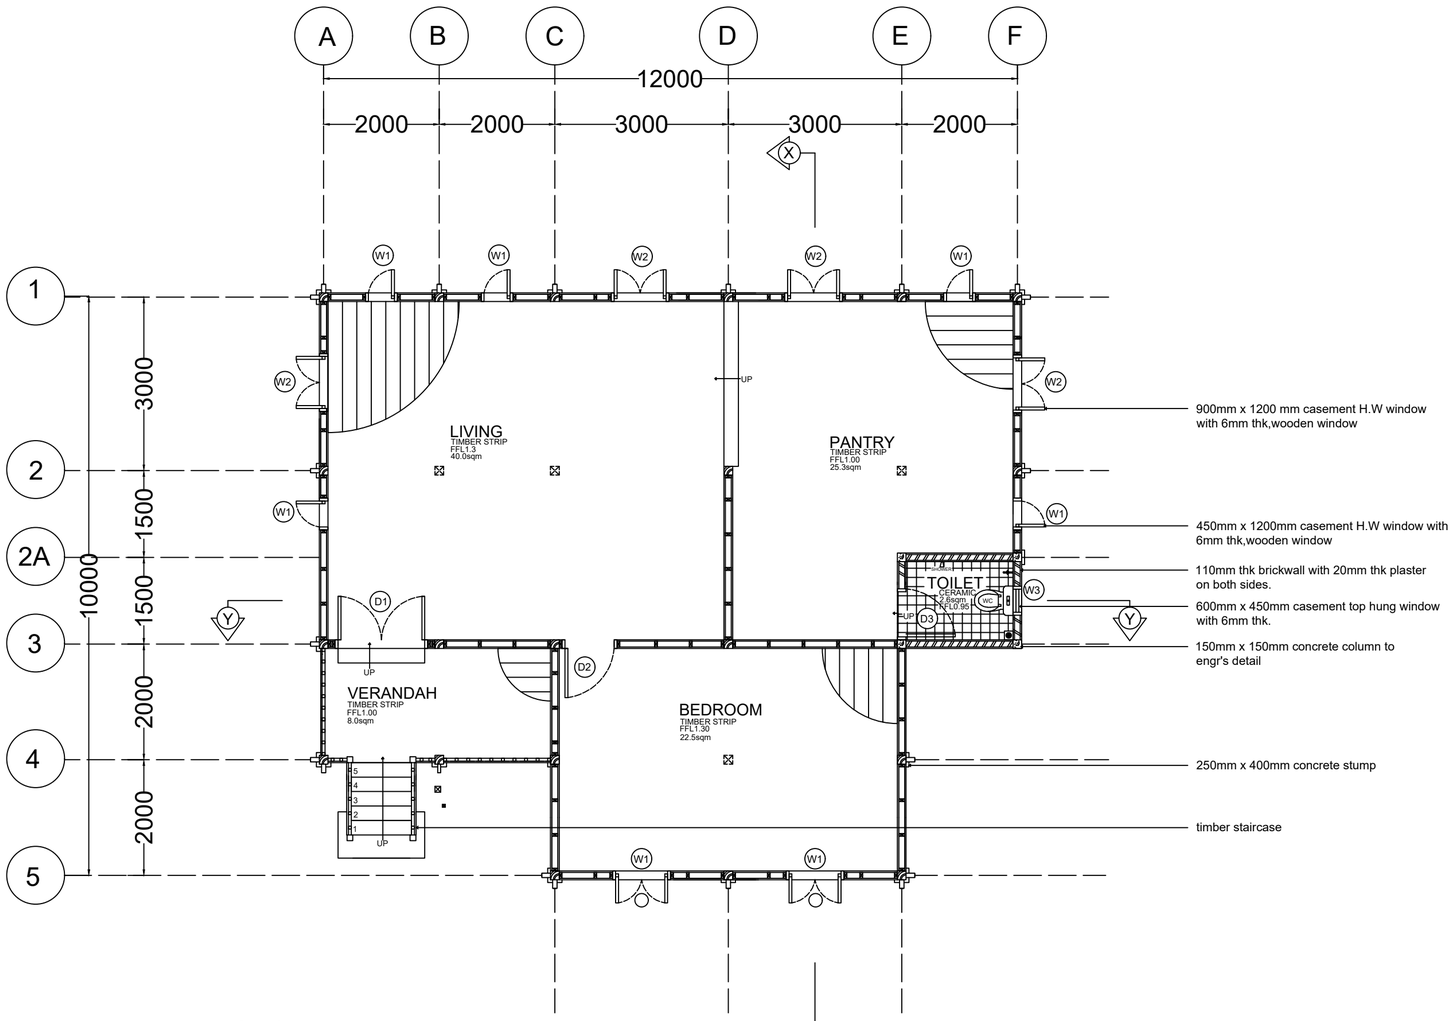

FLOOR PLAN
SCALE 1:75

NAME :
MUHAMMAD DANIAL BIN KASIM

NO MATRIC :
14DSB23F2016

PROJECT TITLE :

SINGLE STOREY TIMBER BUILDING

DRAWING TITLE :

FLOOR PLAN

REMARKS :

DATE :

10 FEBRUARY 2025

SCALE :

1 : 75

CHECKED :

PN NOR AZILLA WATI BINTI ZAMRI

CIK NORAINI BINTI ABU BAKAR

DRAWING NO :

01 / 09

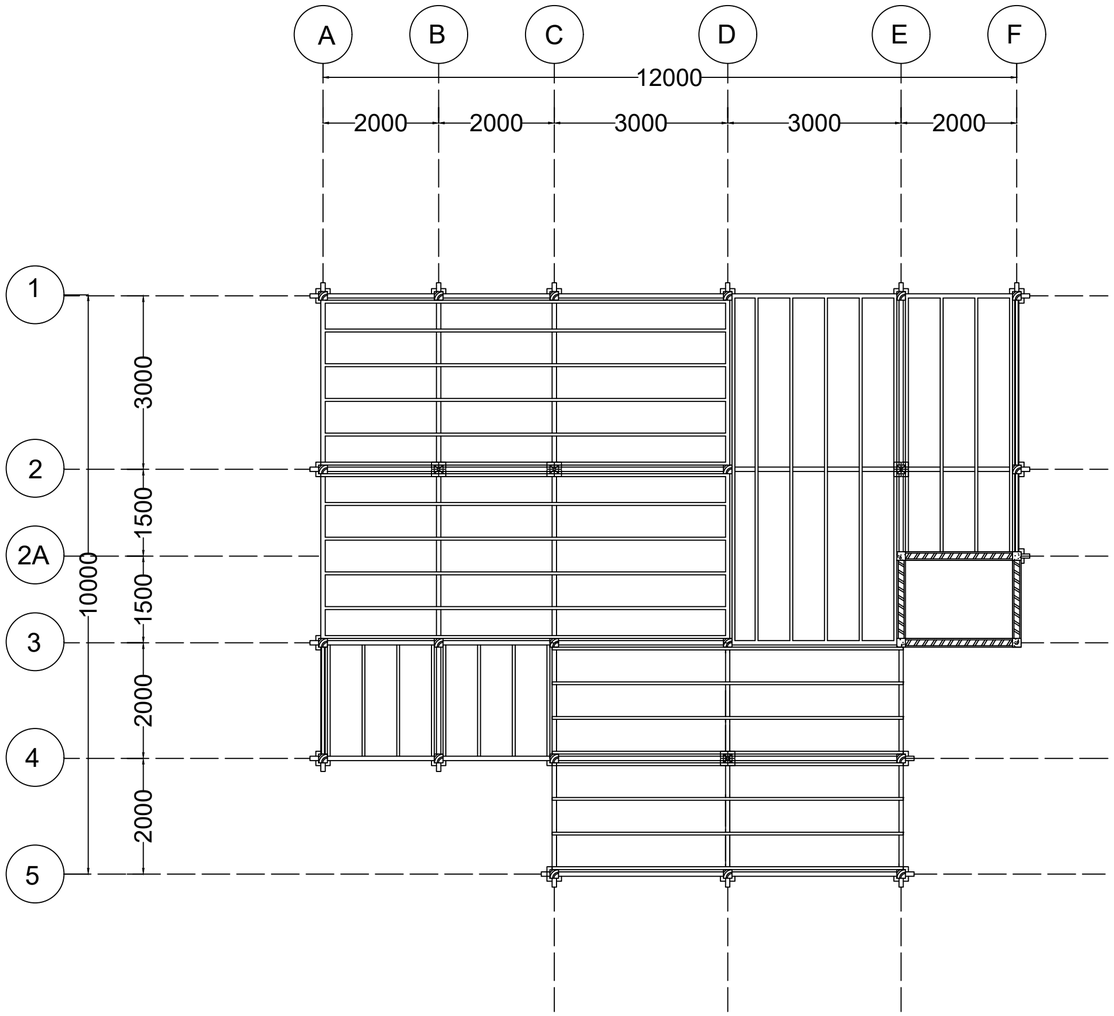

STRUCTURAL PLAN

SCALE 1:75

NAME :
MUHAMMAD DANIAL BIN KASIM

NO MATRIC :
14DSB23F2016

PROJECT TITLE :

SINGLE STOREY TIMBER BUILDING

DRAWING TITLE :

STRUCTURAL

REMARKS :

DATE :

10 FEBRUARY 2025

SCALE :

1 : 75

CHECKED :

PN NOR AZILLA WATI BINTI ZAMRI

CIK NORAINI BINTI ABU BAKAR

DRAWING NO :

02 / 09

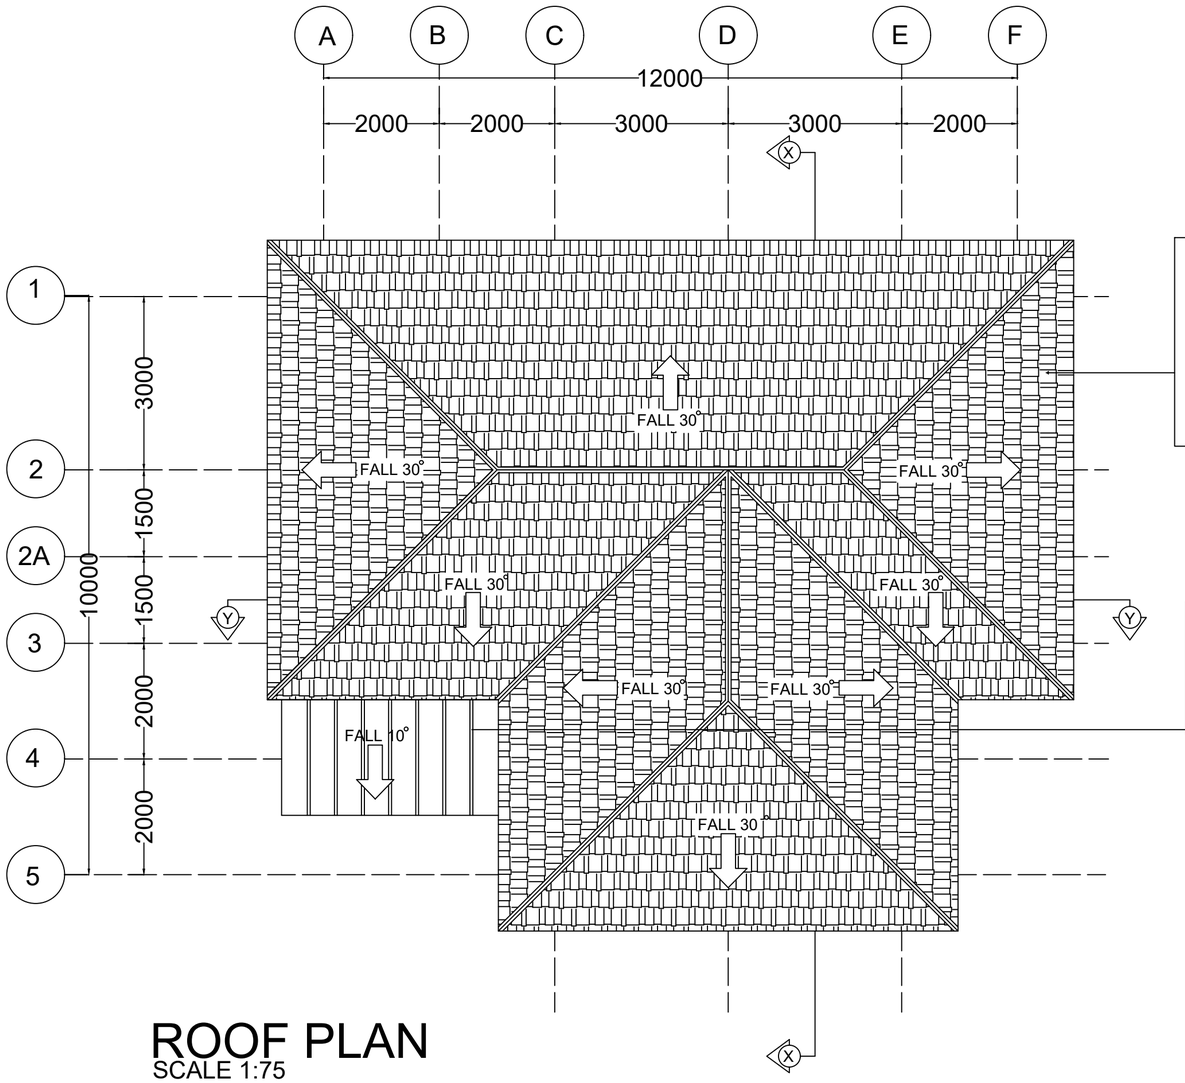

ROOF PLAN
SCALE 1:75

ROOF CONSTRUCTION

concrete roof tiles with ridge cap at 30 degree pitch.Timber batten joint by bolts and nuts to eng's detail25 thk gypsum free flat ceiling to bomba's approval.
-25mm x 50mm H.W batten at 300mm c/c
-50mm x 100mm H.W rafter
-25mm x 25mm thk ceiling joist
-25mm x 200mm H.W fascia board
-75mm x 100mm H.W wall plate
-50mm x 75mm H.W tie beam
-50mm x 100mm H.W strut

ROOF CONSTRUCTION

-roof metal deck at 10 pitch
-25mm x 25mm H.W batten
-25mm x 150mm H.W fascia board
-15mm metal deck
-50mm x 75mm H.W rafter

NAME :
MUHAMMAD DANIAL BIN KASIM

NO MATRIC :
14DSB23F2016

PROJECT TITLE :

SINGLE STOREY TIMBER BUILDING

DRAWING TITLE :

ROOF PLAN

REMARKS :

DATE :

10 FEBRUARY 2025

SCALE :

1 : 75

CHECKED :

PN NOR AZILLA WATI BINTI ZAMRI

CIK NORAINI BINTI ABU BAKAR

DRAWING NO :

03 / 09

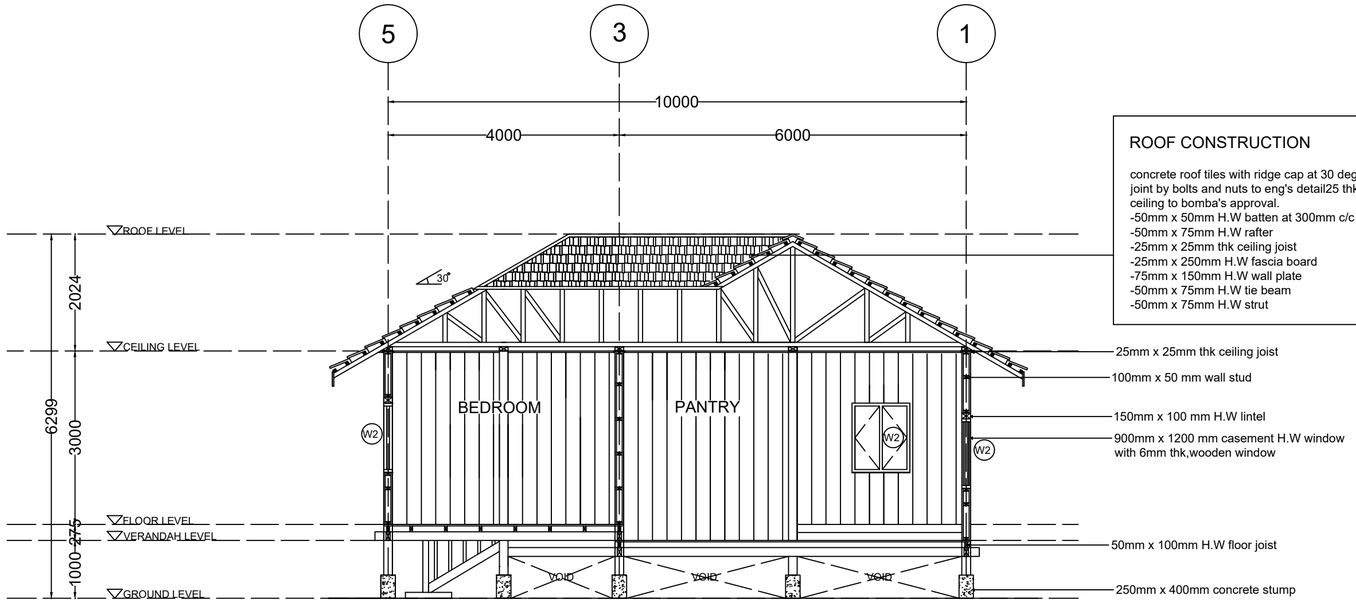

ROOF CONSTRUCTION

concrete roof tiles with ridge cap at 30 degree pitch.Timber batten joint by bolts and nuts to eng's detail25 thk gypsum free flat ceiling to bomba's approval.
-50mm x 50mm H.W batten at 300mm c/c
-50mm x 75mm H.W rafter
-25mm x 25mm thk ceiling joist
-25mm x 250mm H.W fascia board
-75mm x 150mm H.W wall plate
-50mm x 75mm H.W tie beam
-50mm x 75mm H.W strut

SECTION X-X
SCALE 1:75

NAME :
MUHAMMAD DANIAL BIN KASIM

NO MATRIC :
14DSB23F2016

PROJECT TITLE :

SINGLE STOREY TIMBER BUILDING

DRAWING TITLE :

SECTION X-X

REMARKS :

DATE :

10 FEBRUARY 2025

SCALE :

1 : 75

CHECKED :

PN NOR AZILLA WATI BINTI ZAMRI

CIK NORAINI BINTI ABU BAKAR

DRAWING NO :

04 / 09

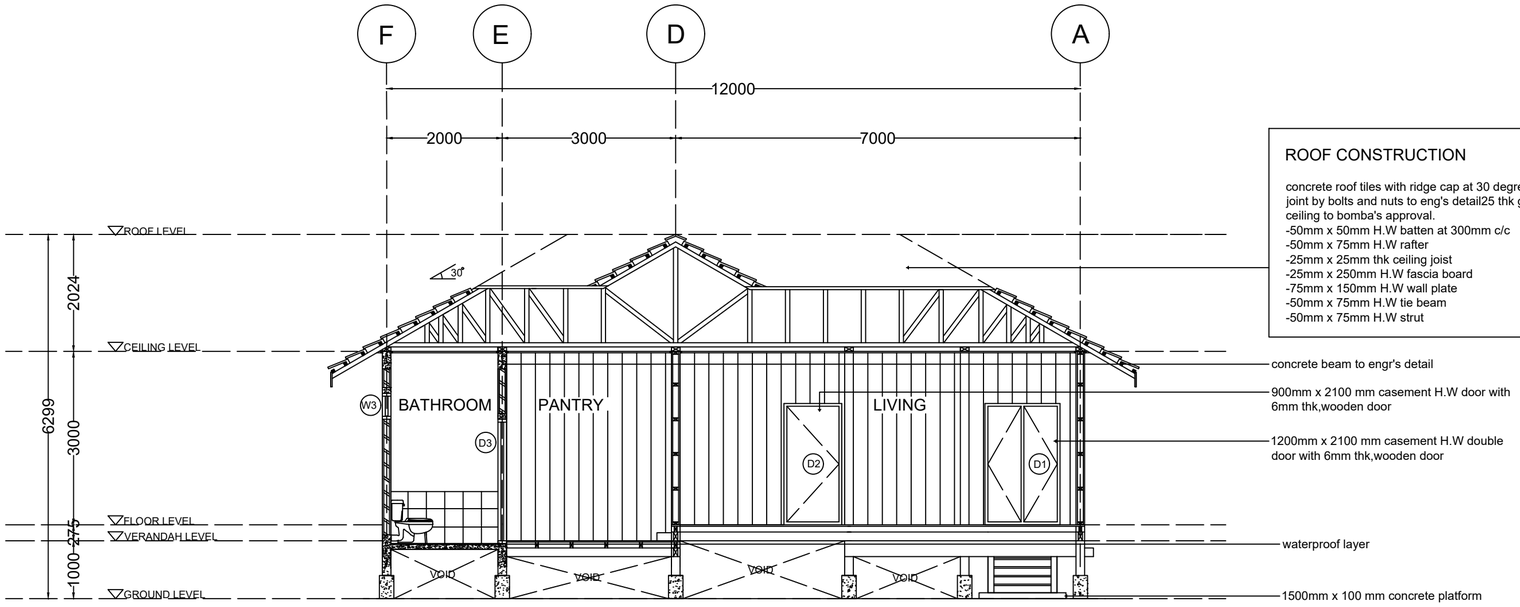

SECTION Y-Y
SCALE 1:75

ROOF CONSTRUCTION

concrete roof tiles with ridge cap at 30 degree pitch.Timber batten joint by bolts and nuts to eng's detail25 thk gypsum free flat ceiling to bomba's approval.
-50mm x 50mm H.W batten at 300mm c/c
-50mm x 75mm H.W rafter
-25mm x 25mm thk ceiling joist
-25mm x 250mm H.W fascia board
-75mm x 150mm H.W wall plate
-50mm x 75mm H.W tie beam
-50mm x 75mm H.W strut

NAME :
MUHAMMAD DANIAL BIN KASIM

NO MATRIC :
14DSB23F2016

PROJECT TITLE :

SINGLE STOREY TIMBER BUILDING

DRAWING TITLE :

SECTION Y-Y

REMARKS :

DATE :

10 FEBRUARY 2025

SCALE :

1 : 75

CHECKED :

PN NOR AZILLA WATI BINTI ZAMRI

CIK NORAINI BINTI ABU BAKAR

DRAWING NO :

05 / 09

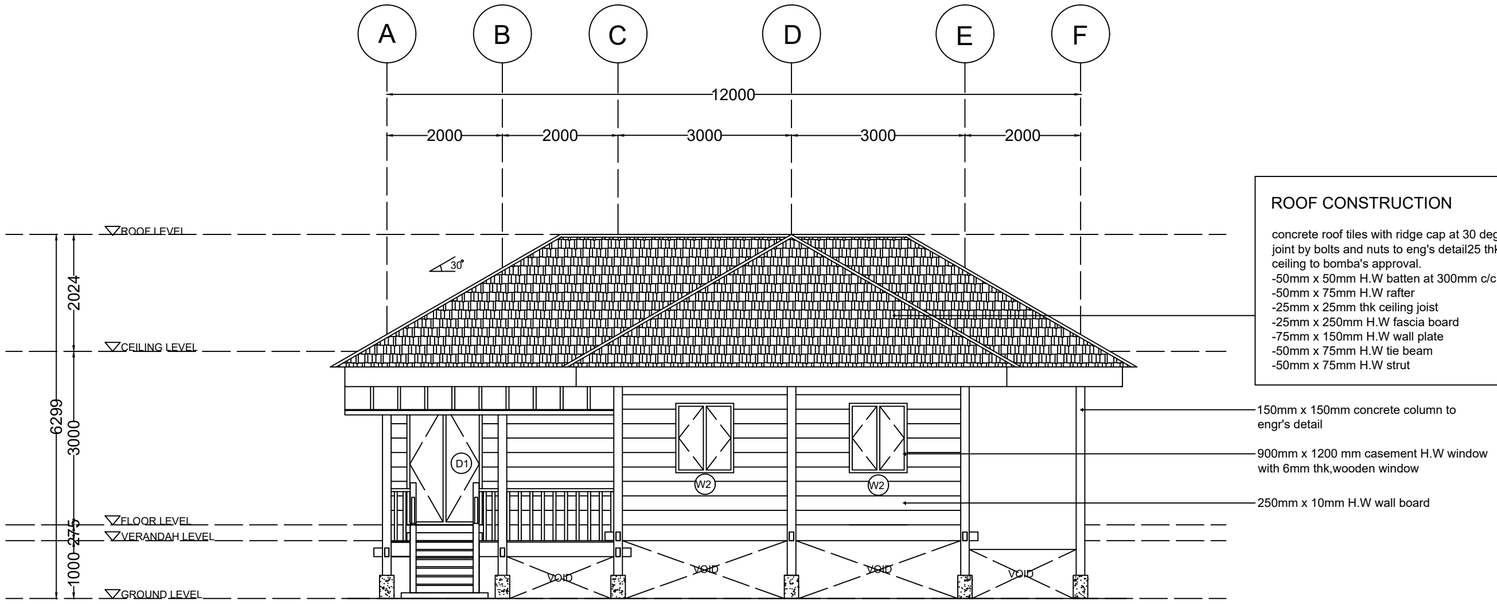

ROOF CONSTRUCTION

concrete roof tiles with ridge cap at 30 degree pitch.Timber batten joint by bolts and nuts to eng's detail25 thk gypsum free flat ceiling to bomba's approval.
-50mm x 50mm H.W batten at 300mm c/c
-50mm x 75mm H.W rafter
-25mm x 25mm thk ceiling joist
-25mm x 250mm H.W fascia board
-75mm x 150mm H.W wall plate
-50mm x 75mm H.W tie beam
-50mm x 75mm H.W strut

FRONT ELEVATION
SCALE 1:75

NAME :
MUHAMMAD DANIAL BIN KASIM

NO MATRIC :
14DSB23F2016

PROJECT TITLE :

SINGLE STOREY TIMBER BUILDING

DRAWING TITLE :

FRONT ELEVATION

REMARKS :

DATE :

10 FEBRUARY 2025

SCALE :

1 : 75

CHECKED :

PN NOR AZILLA WATI BINTI ZAMRI

CIK NORAINI BINTI ABU BAKAR

DRAWING NO :

06 / 09

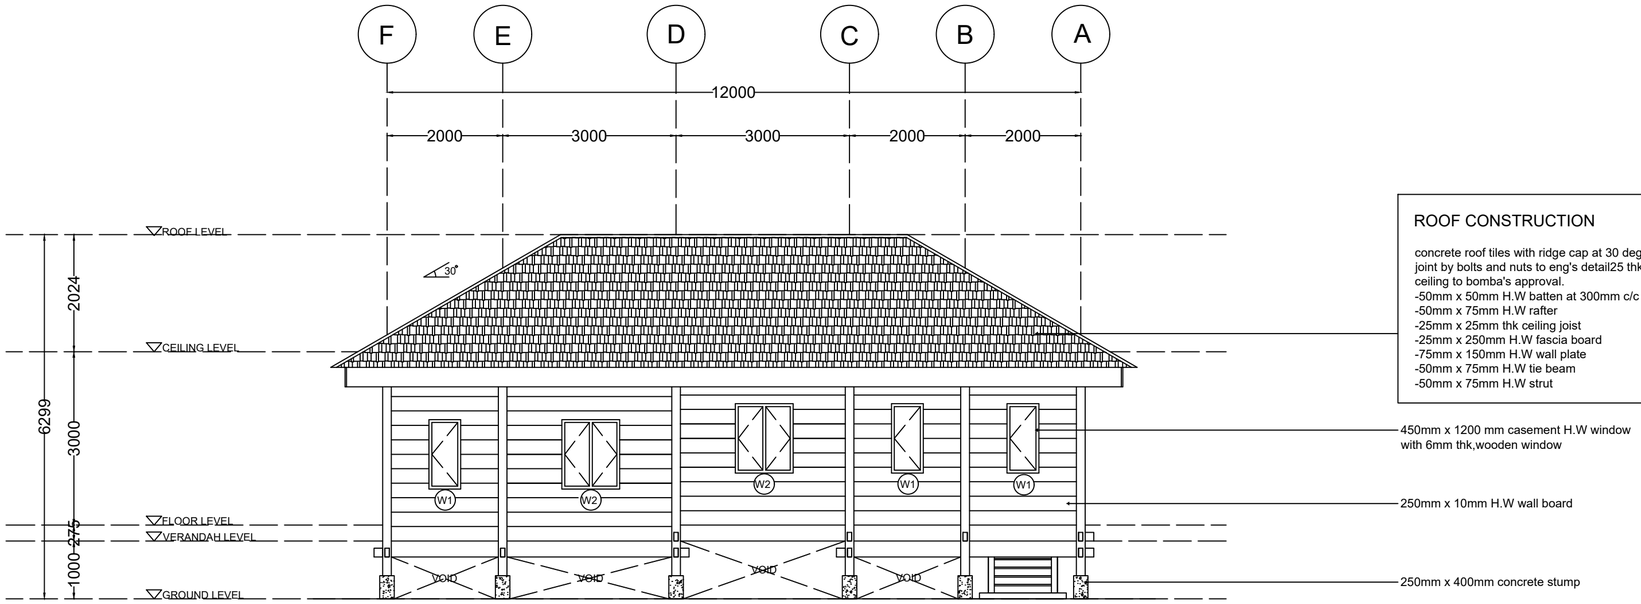

REAR ELEVATION
SCALE 1:75

ROOF CONSTRUCTION

concrete roof tiles with ridge cap at 30 degree pitch.Timber batten joint by bolts and nuts to eng's detail25 thk gypsum free flat ceiling to bomba's approval.
-50mm x 50mm H.W batten at 300mm c/c
-50mm x 75mm H.W rafter
-25mm x 25mm thk ceiling joist
-25mm x 250mm H.W fascia board
-75mm x 150mm H.W wall plate
-50mm x 75mm H.W tie beam
-50mm x 75mm H.W strut

450mm x 1200 mm casement H.W window with 6mm thk,wooden window

250mm x 10mm H.W wall board

250mm x 400mm concrete stump

NAME :
MUHAMMAD DANIAL BIN KASIM

NO MATRIC :
14DSB23F2016

PROJECT TITLE :

SINGLE STOREY TIMBER BUILDING

DRAWING TITLE :

REAR ELEVATION

REMARKS :

DATE :

10 FEBRUARY 2025

SCALE :

1 : 75

CHECKED :

PN NOR AZILLA WATI BINTI ZAMRI

CIK NORAINI BINTI ABU BAKAR

DRAWING NO :

07 / 09

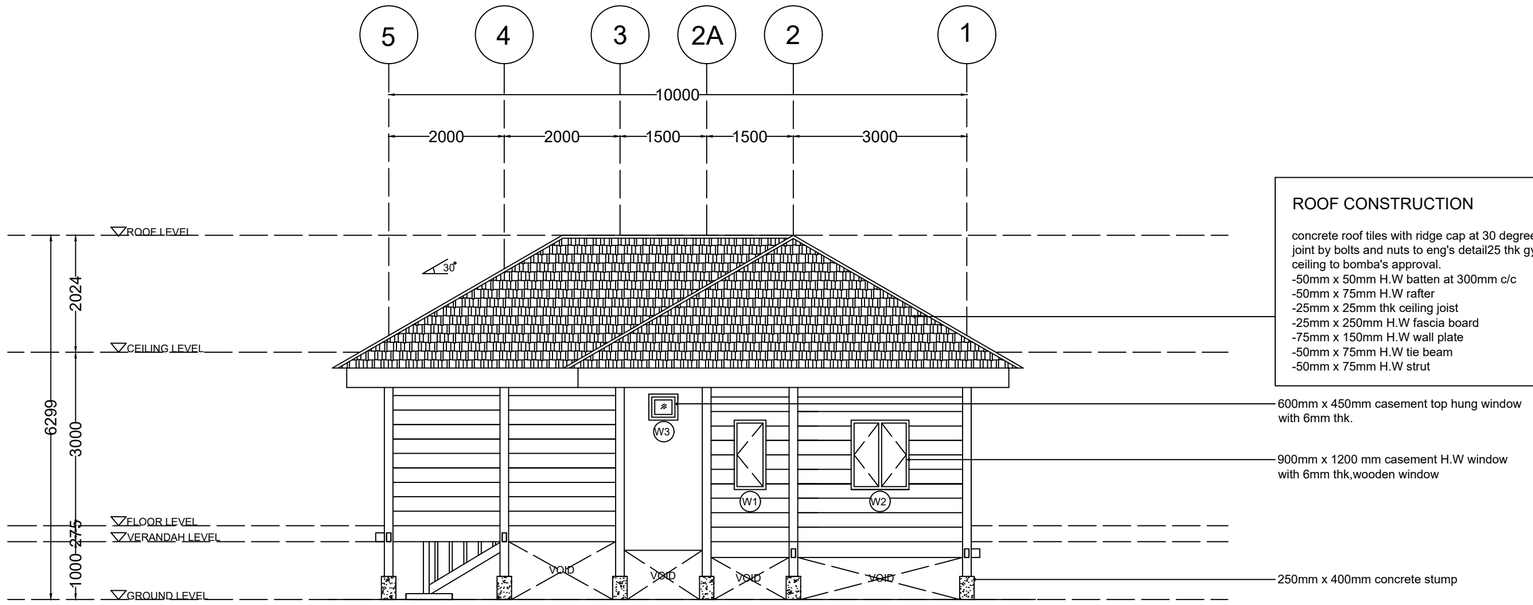

ROOF CONSTRUCTION

concrete roof tiles with ridge cap at 30 degree pitch.Timber batten joint by bolts and nuts to eng's detail25 thk gypsum free flat ceiling to bomba's approval.
-50mm x 50mm H.W batten at 300mm c/c
-50mm x 75mm H.W rafter
-25mm x 25mm thk ceiling joist
-25mm x 250mm H.W fascia board
-75mm x 150mm H.W wall plate
-50mm x 75mm H.W tie beam
-50mm x 75mm H.W strut

RIGHT ELEVATION

SCALE 1:75

NAME :
MUHAMMAD DANIAL BIN KASIM

NO MATRIC :
14DSB23F2016

PROJECT TITLE :

SINGLE STOREY TIMBER BUILDING

DRAWING TITLE :

RIGHT ELEVATION

REMARKS :

DATE :

10 FEBRUARY 2025

SCALE :

1 : 75

CHECKED :

PN NOR AZILLA WATI BINTI ZAMRI

CIK NORAINI BINTI ABU BAKAR

DRAWING NO :

08 / 09

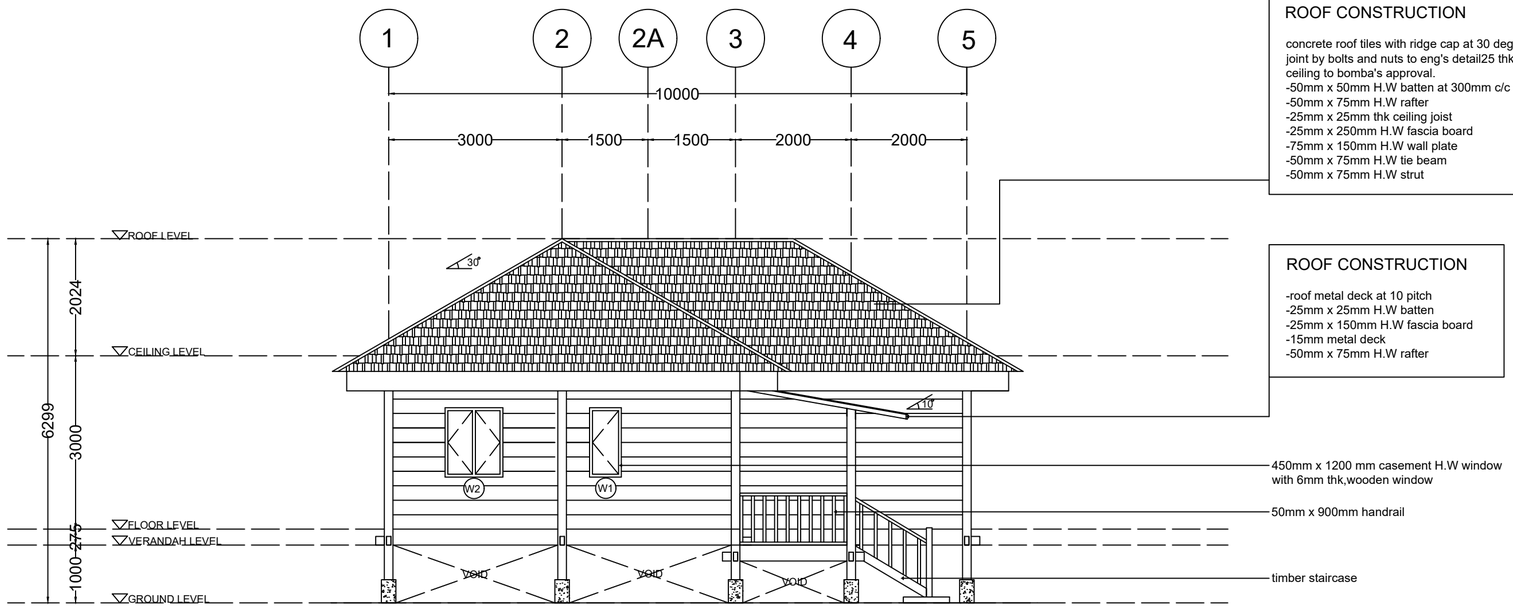

LEFT ELEVATION

SCALE 1:75

NAME :
MUHAMMAD DANIAL BIN KASIM

NO MATRIC :
14DSB23F2016

PROJECT TITLE :

SINGLE STOREY TIMBER BUILDING

DRAWING TITLE :

LEFT ELEVATION

REMARKS :

DATE :

10 FEBRUARY 2025

SCALE :

1 : 75

CHECKED :

PN NOR AZILLA WATI BINTI ZAMRI

CIK NORAINI BINTI ABU BAKAR

DRAWING NO :

09 / 09